


Liegenschaftskarte

Erstellt: 16.06.2025

Maßstab: 1:500

Flurstück: 9495
Gemarkung: Sindelfingen

Gemeinde: Sindelfingen
Kreis: Böblingen
Bundesland: Baden-Württemberg

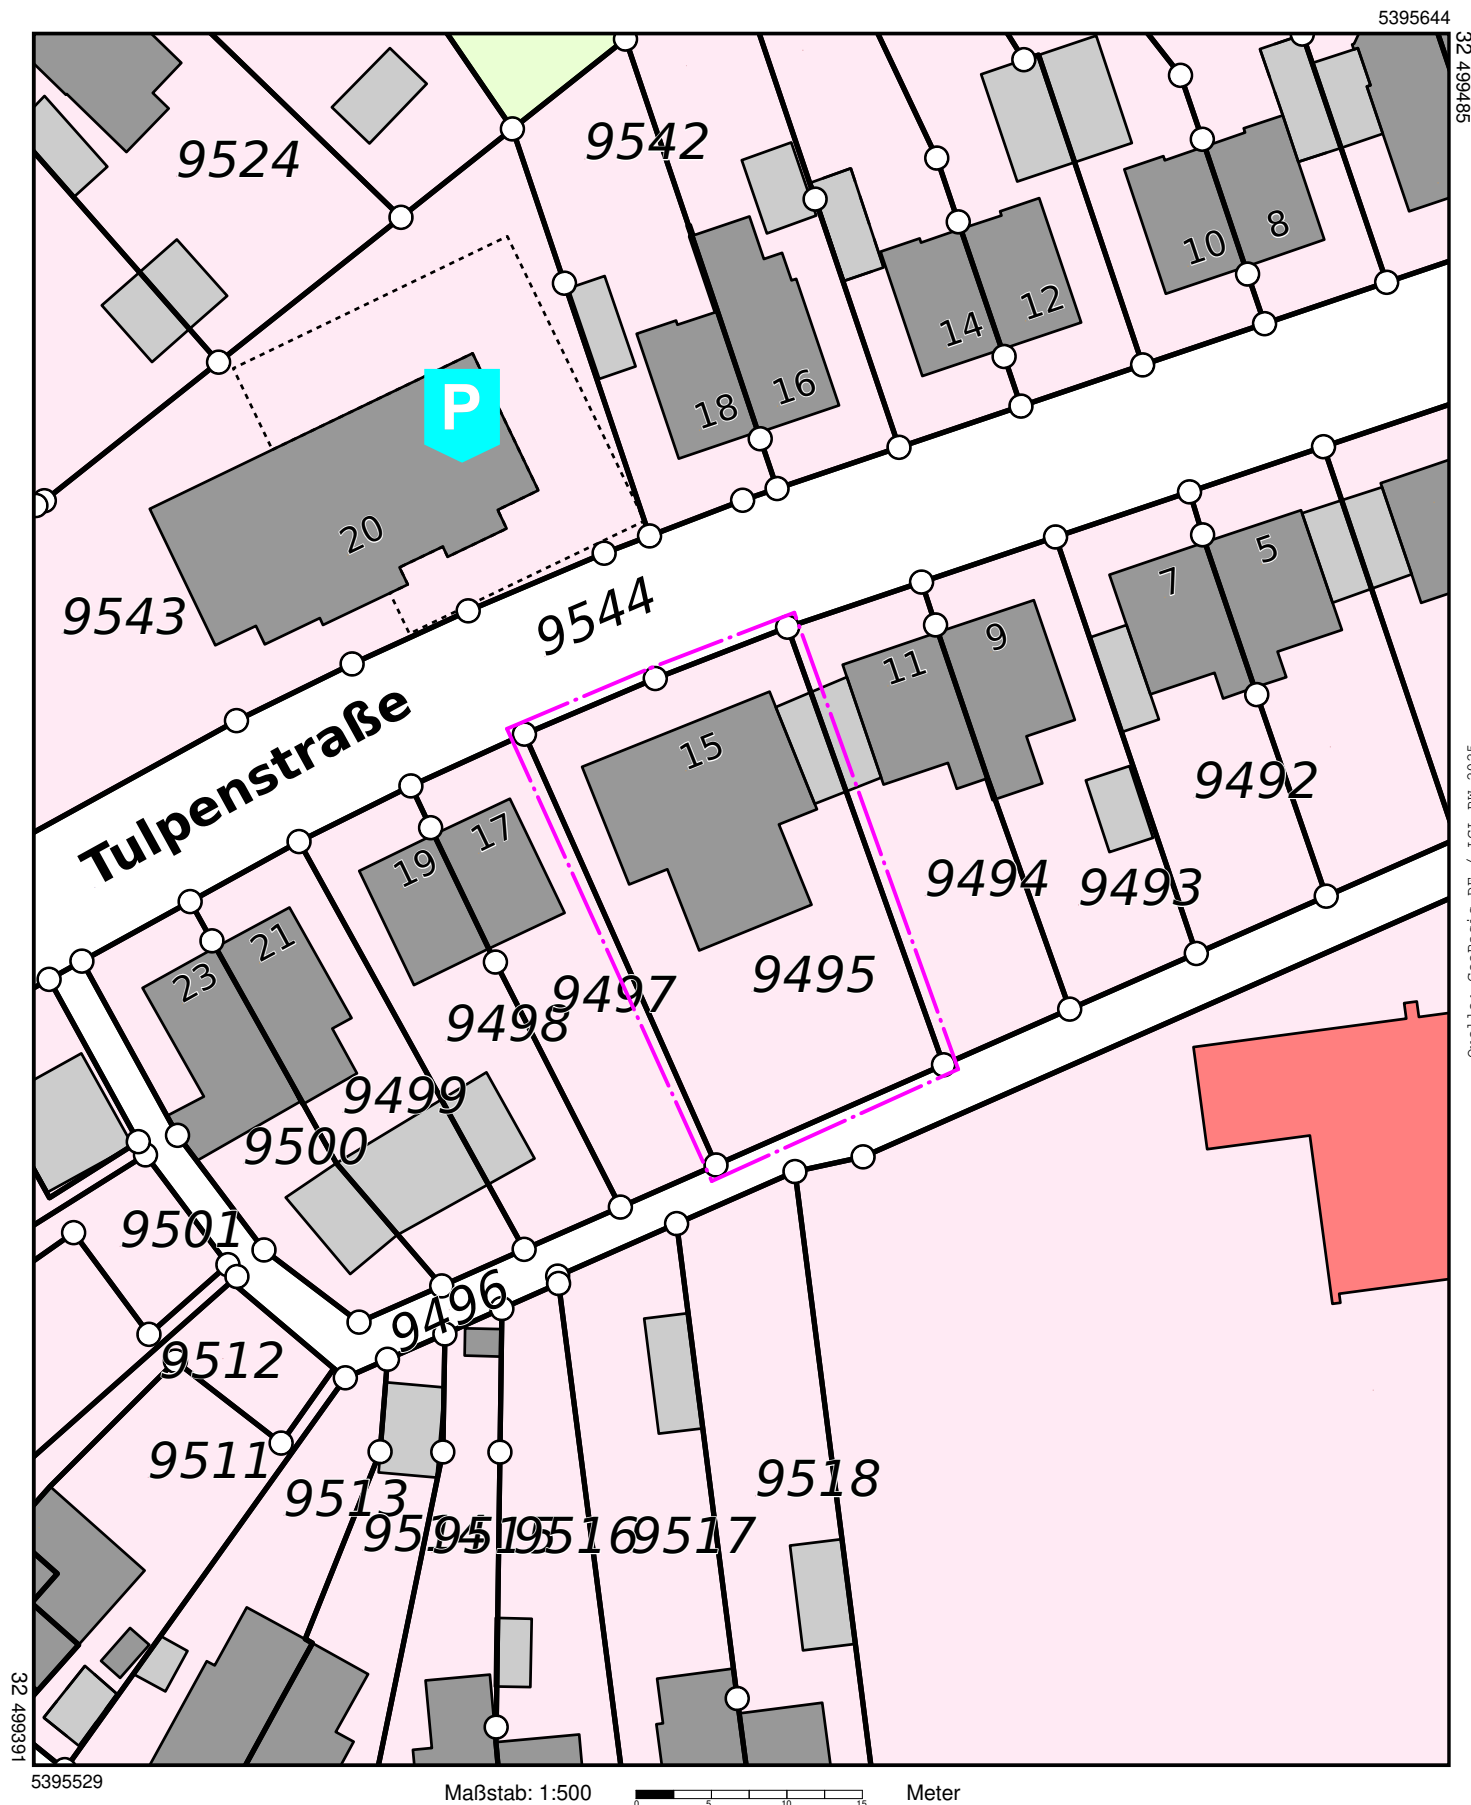

Quelle: GeoBasis-DE / LGL-BW 2025

AUFTEILUNGSPLANUNG

Lageplan

Art und Ort des Vorhabens: Aufteilung eines bestehenden Wohngebäudes mit 6 Wohneinheiten und 1 Garage und 6 PKW Außenstellplätze
Tulpenstraße 15
71063 Sindelfingen
Flst.-Nr.: 9495

Bauherr u. Antragsteller: Württemberger Wohnkonzepte GmbH
Ziegelstraße 1
73230 Kirchheim unter Teck
Vertreten durch die Geschäftsführung:
Dorothee Hahn & Marco Hans



Entwurfsverfasser: **jps architects**
Jean Pierre Schellhaas
Architekt
Krokusstraße 3
71034 Böblingen
Mitglied der AKBW
jp@jps-architects.com
0157 / 39 22 86 22



Handwritten signatures: Dorothee Hahn, Marco Hans, and Jean Pierre Schellhaas.

Planstand: 04.08.2025

M 1:100

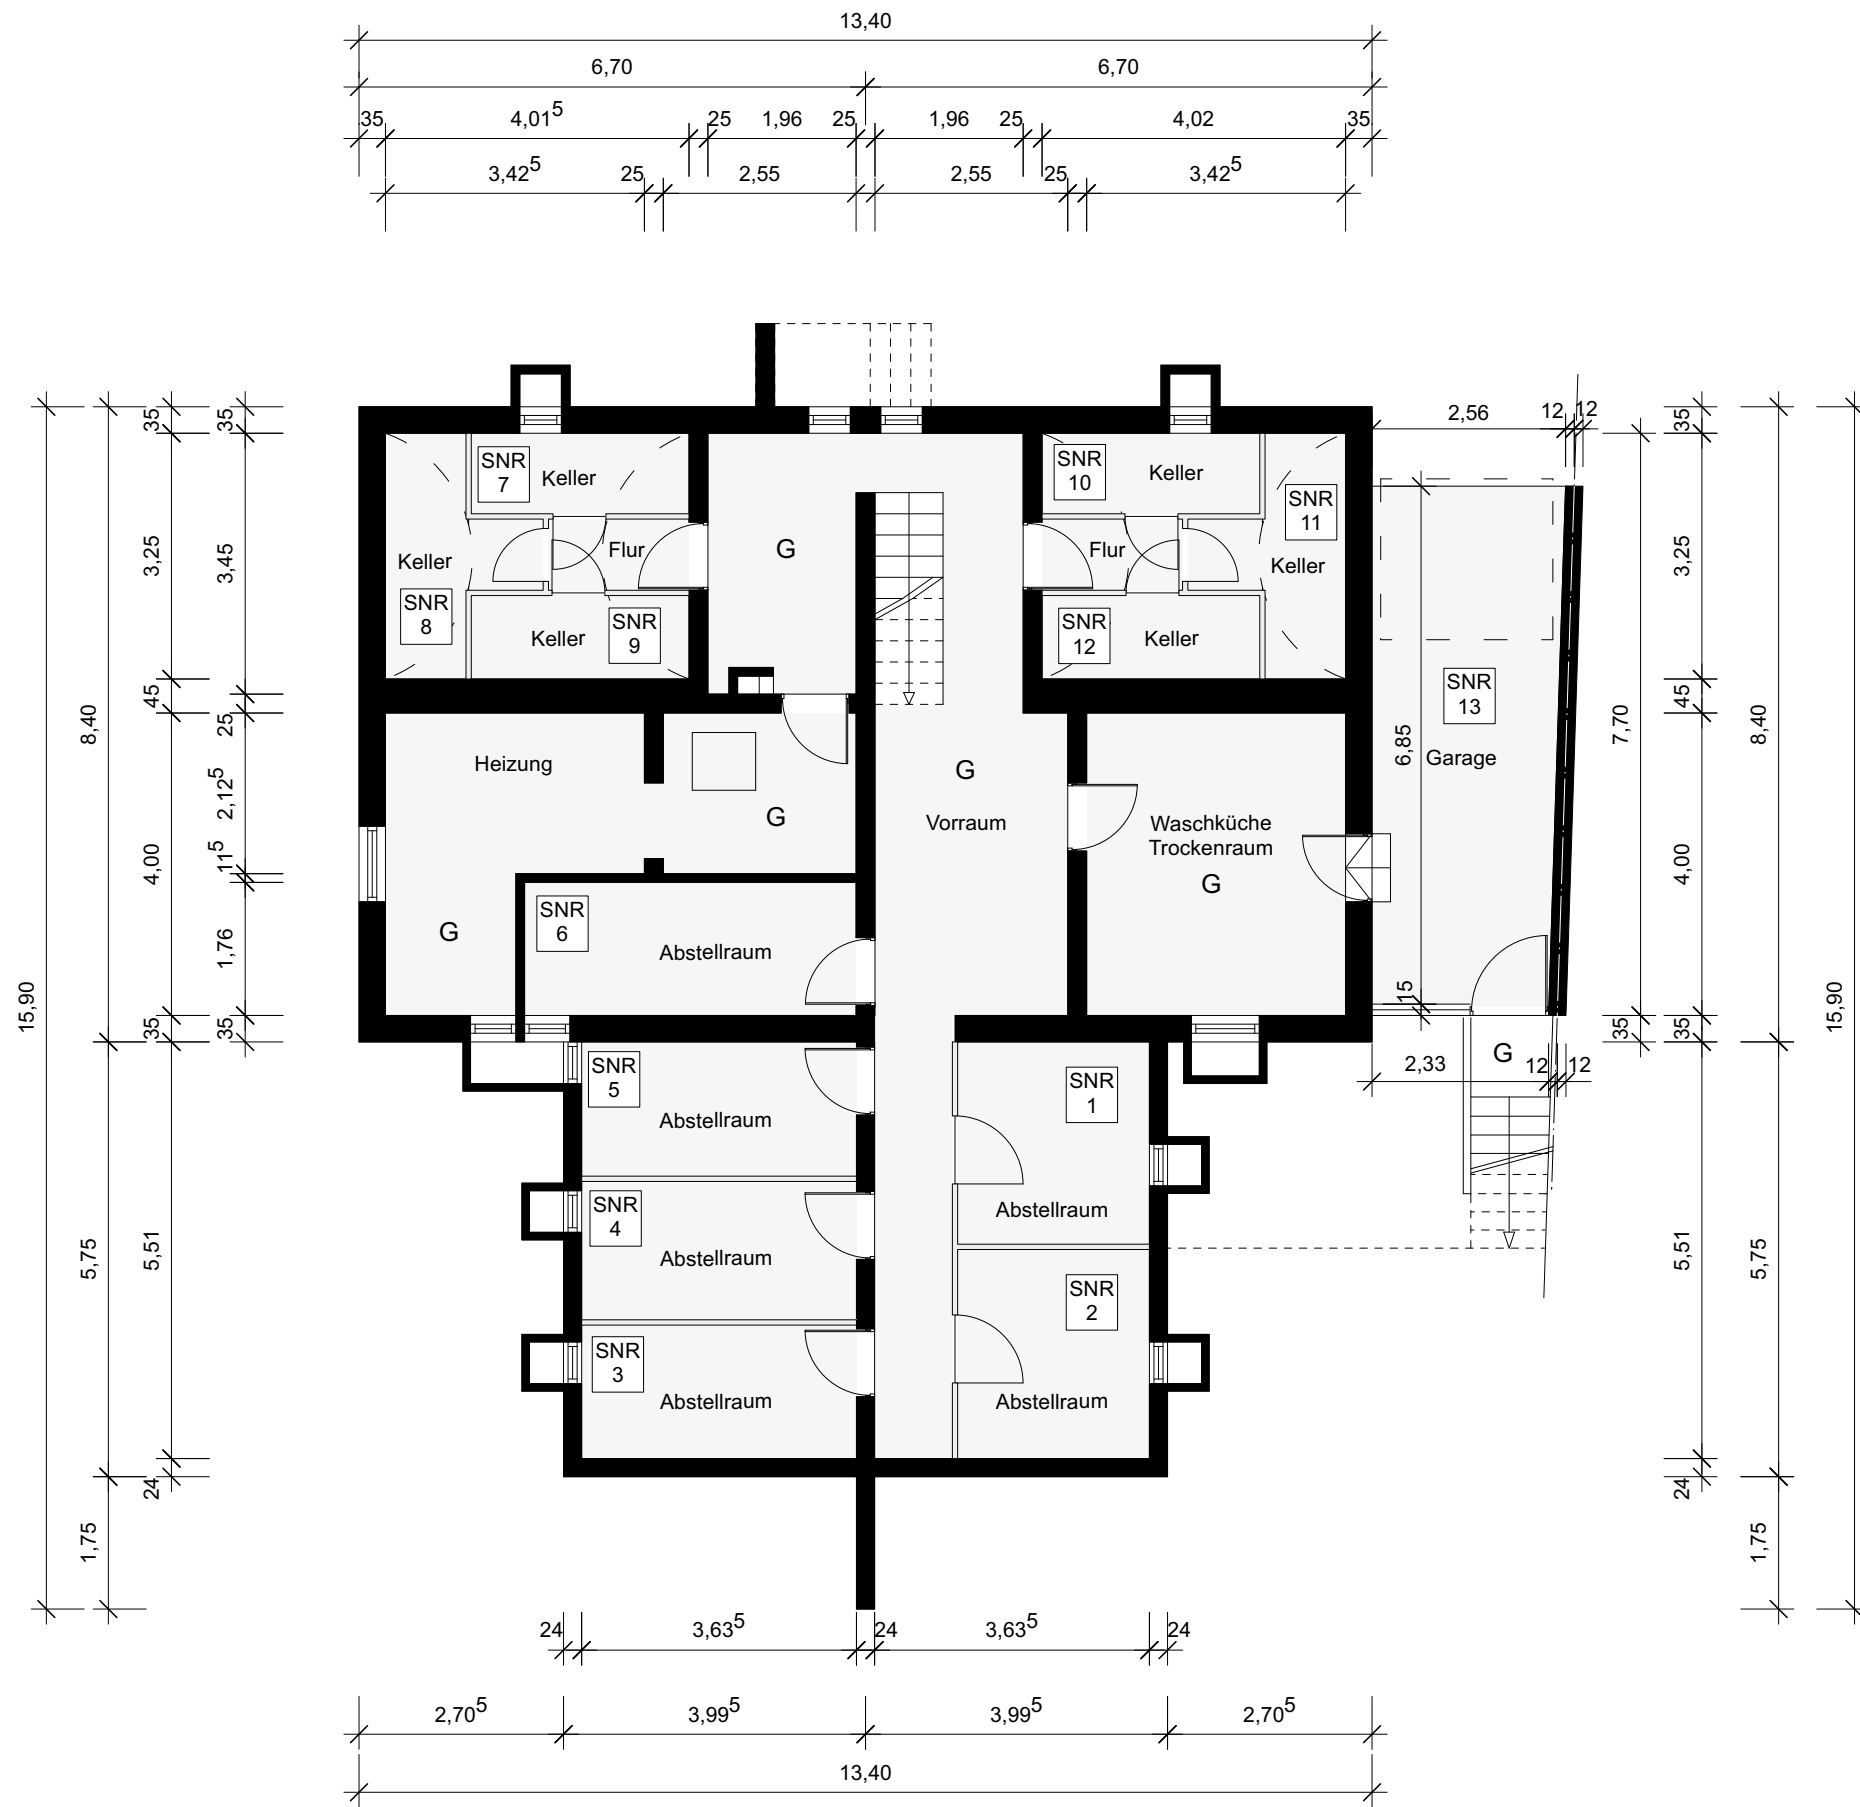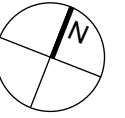

AUFTEILUNGSPLANUNG

Untergeschoss

Art und Ort des Vorhabens: Aufteilung eines bestehenden Wohngebäudes mit 6 Wohneinheiten und 1 Garage und 6 PKW Außenstellplätze
Tulpenstraße 15
71063 Sindelfingen
Flst.-Nr.: 9495

Bauherr u. Antragsteller: Württemberger Wohnkonzepte GmbH
Ziegelstraße 1
73230 Kirchheim unter Teck
Vertreten durch die Geschäftsführung:
Dorothee Hahn & Marco Hans

Entwurfsverfasser: **jps architects**
Jean Pierre Schellhaas
Architekt
Krokusstraße 3
71034 Böblingen
Mitglied der AKBW





jp@jps-architects.com
0157 / 39 22 86 22



J. Pierre Schellhaas

Planstand: 04.08.2025

M 1:100

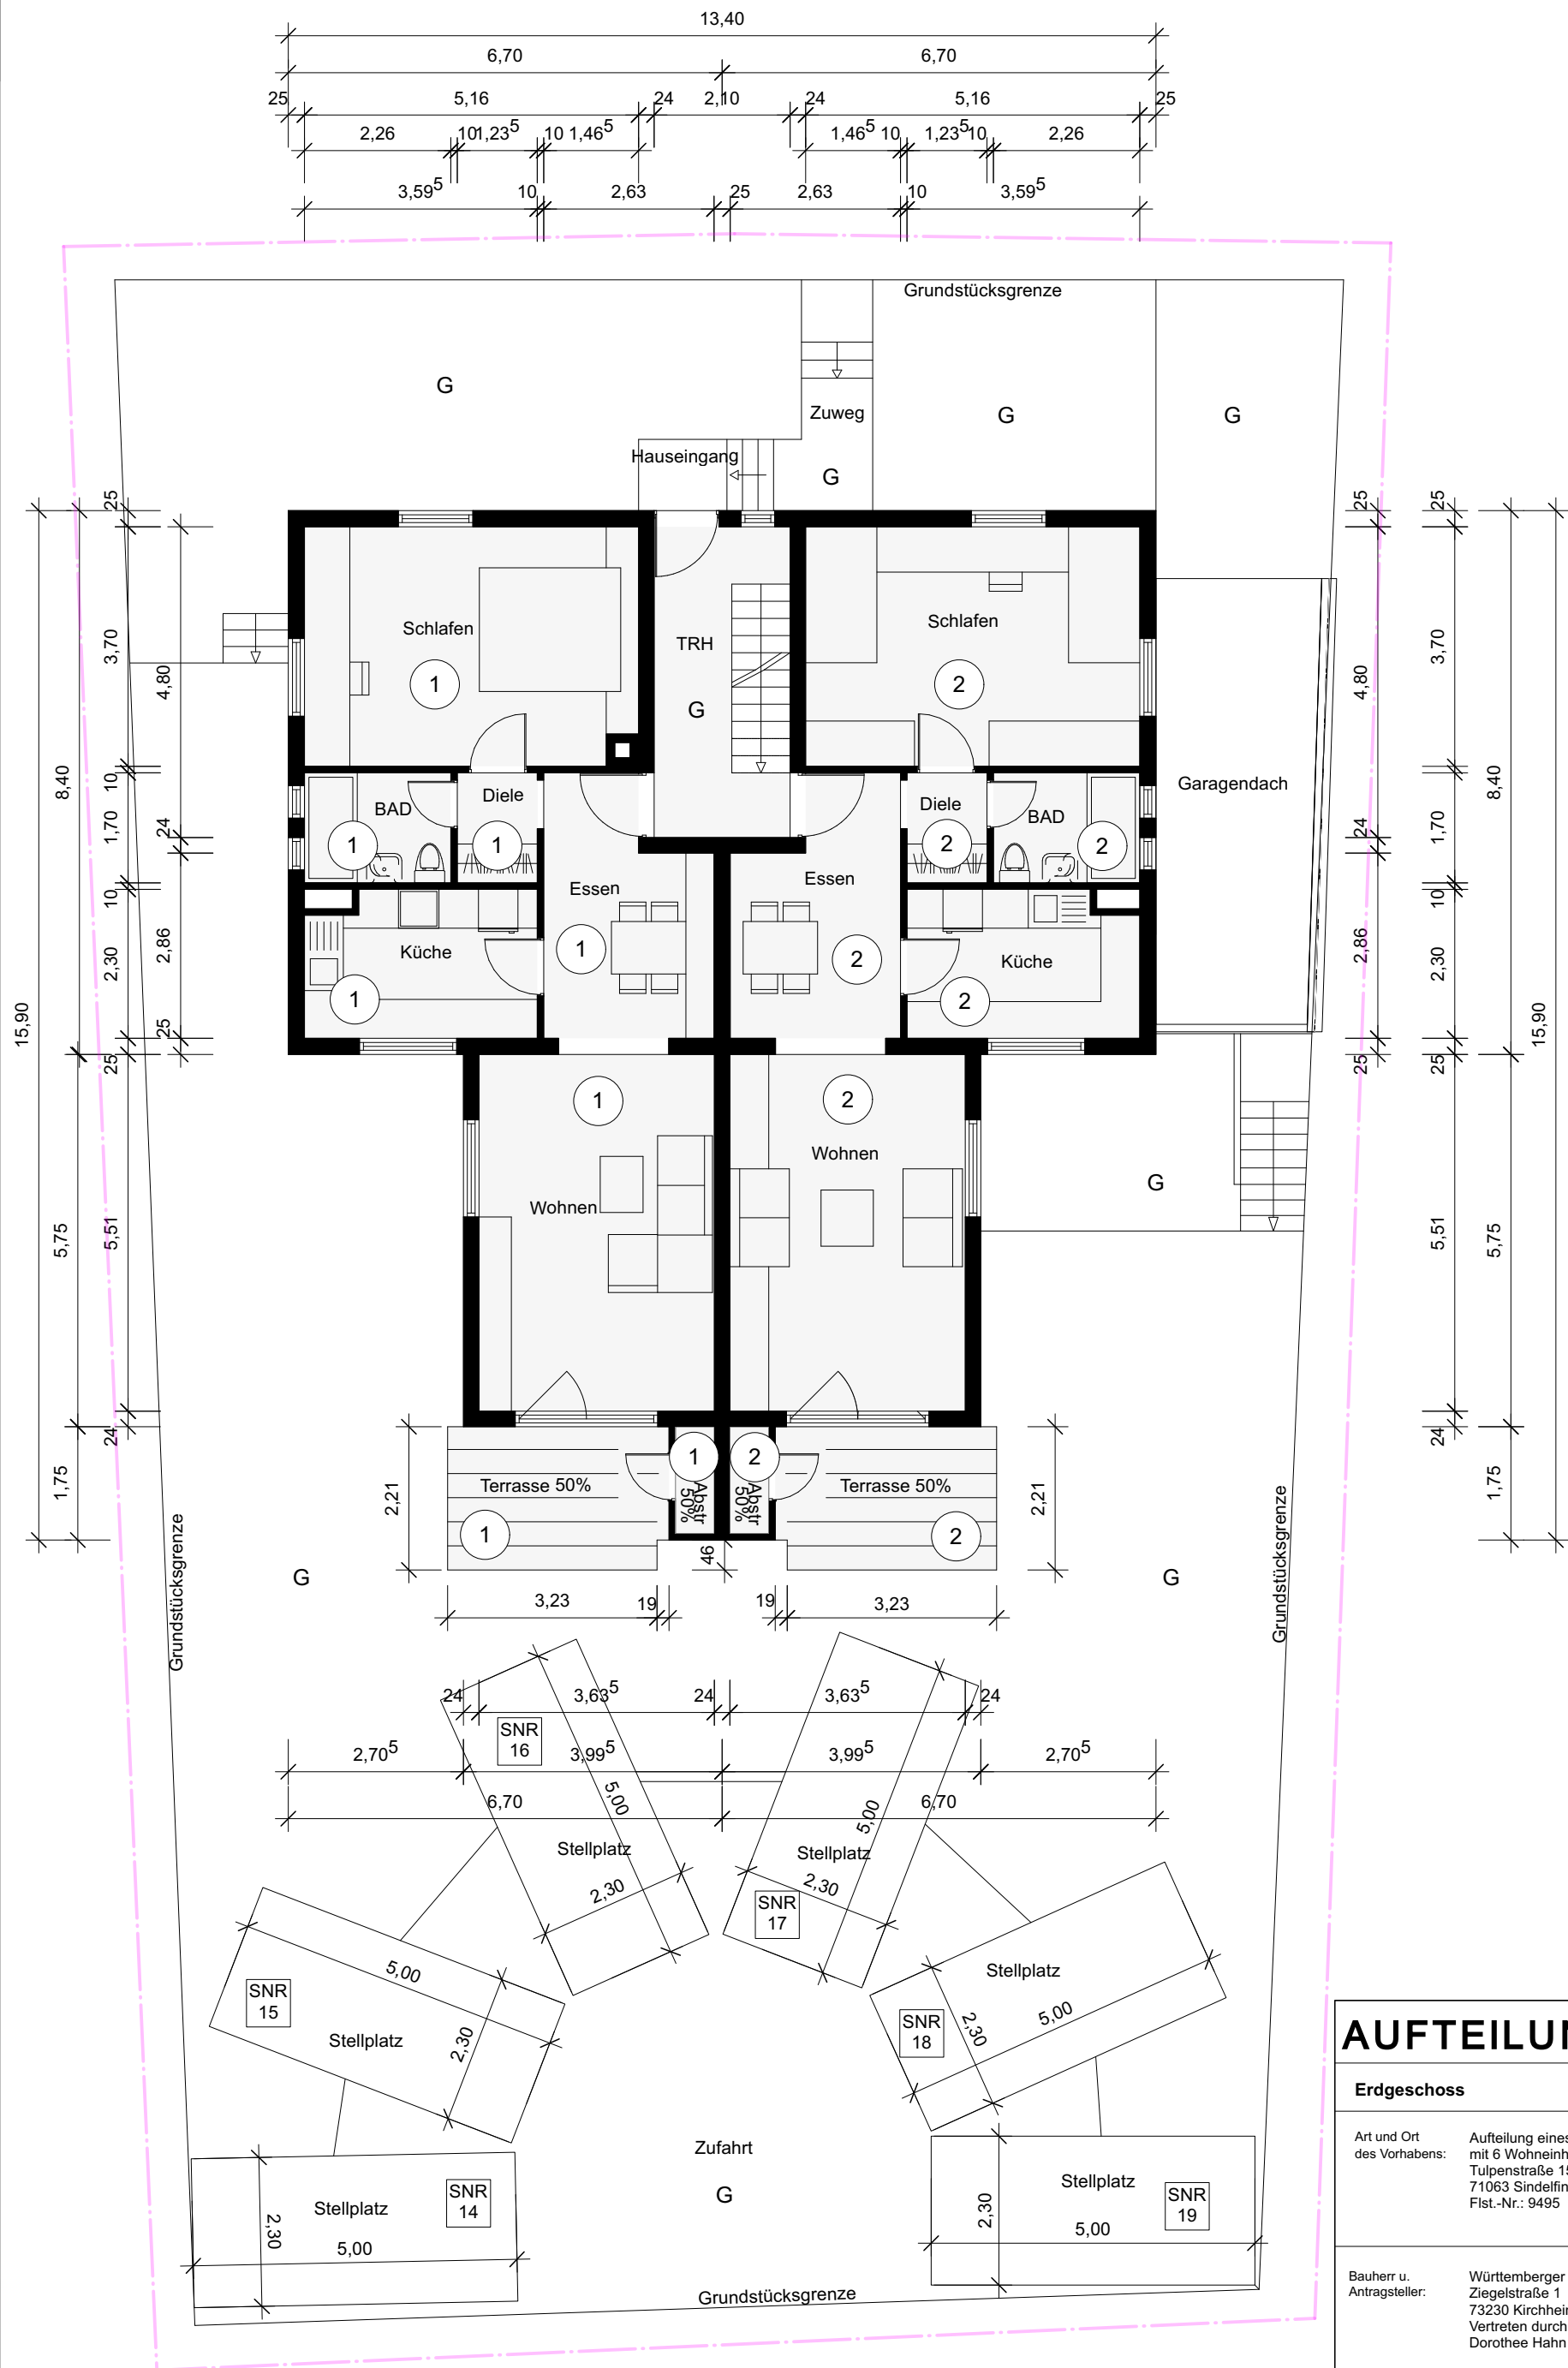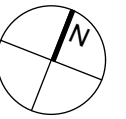

AUFTEILUNGSPLANUNG	
Erdgeschoss	
Art und Ort des Vorhabens:	Aufteilung eines bestehenden Wohngebäudes mit 6 Wohneinheiten und 1 Garage und 6 PKW Außenstellplätze Tulpenstraße 15 71063 Sindelfingen Flst.-Nr.: 9495
Bauherr u. Antragsteller:	Württembergischer Wohnkonzepte GmbH Ziegelstraße 1 73230 Kirchheim unter Teck Vertreten durch die Geschäftsführung: Dorothee Hahn & Marco Hans
Entwurfsverfasser:	jps architects Jean Pierre Schellhaas Architekt Krokusstraße 3 71034 Böblingen Mitglied der AKBW jp@jps-architects.com 0157 / 39 22 86 22
Planstand: 04.08.2025	
M 1:100	

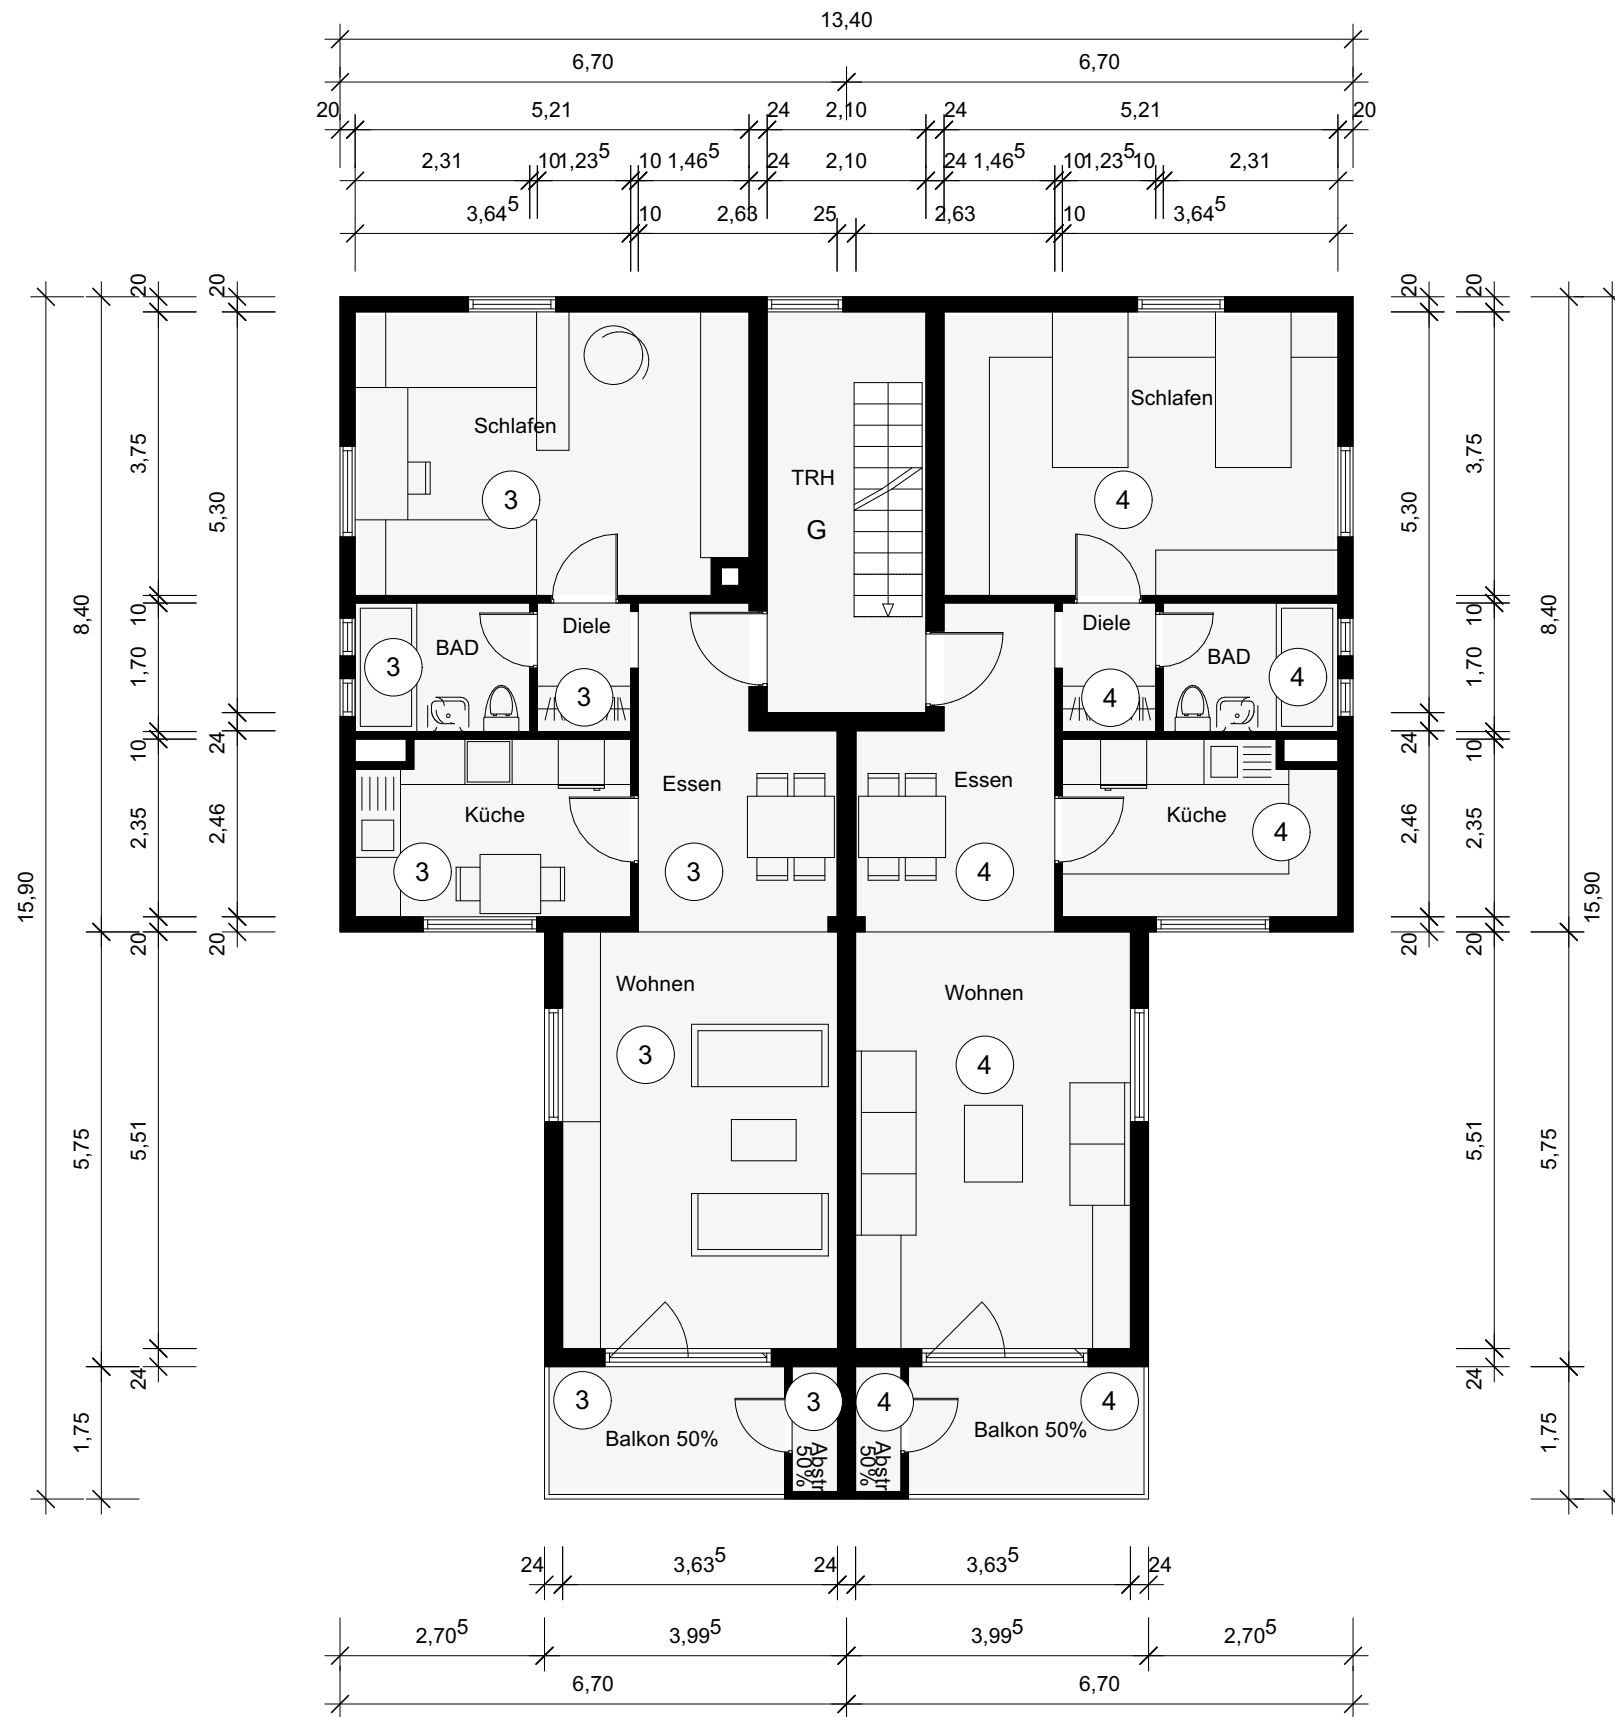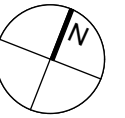

AUFTEILUNGSPLANUNG

Obergeschoss

Art und Ort des Vorhabens: Aufteilung eines bestehenden Wohngebäudes mit 6 Wohneinheiten und 1 Garage und 6 PKW Außenstellplätze
Tulpenstraße 15
71063 Sindelfingen
Flst.-Nr.: 9495

Bauherr u. Antragsteller: Württemberger Wohnkonzepte GmbH
Ziegelstraße 1
73230 Kirchheim unter Teck
Vertreten durch die Geschäftsführung:
Dorothee Hahn & Marco Hans


Entwurfsverfasser: **jps architects**
Jean Pierre Schellhaas
Architekt
Krokusstraße 3
71034 Böblingen
Mitglied der AKBW
jp@jps-architects.com
0157 / 39 22 86 22



J. Pierre Schellhaas

Planstand: 04.08.2025

M 1:100

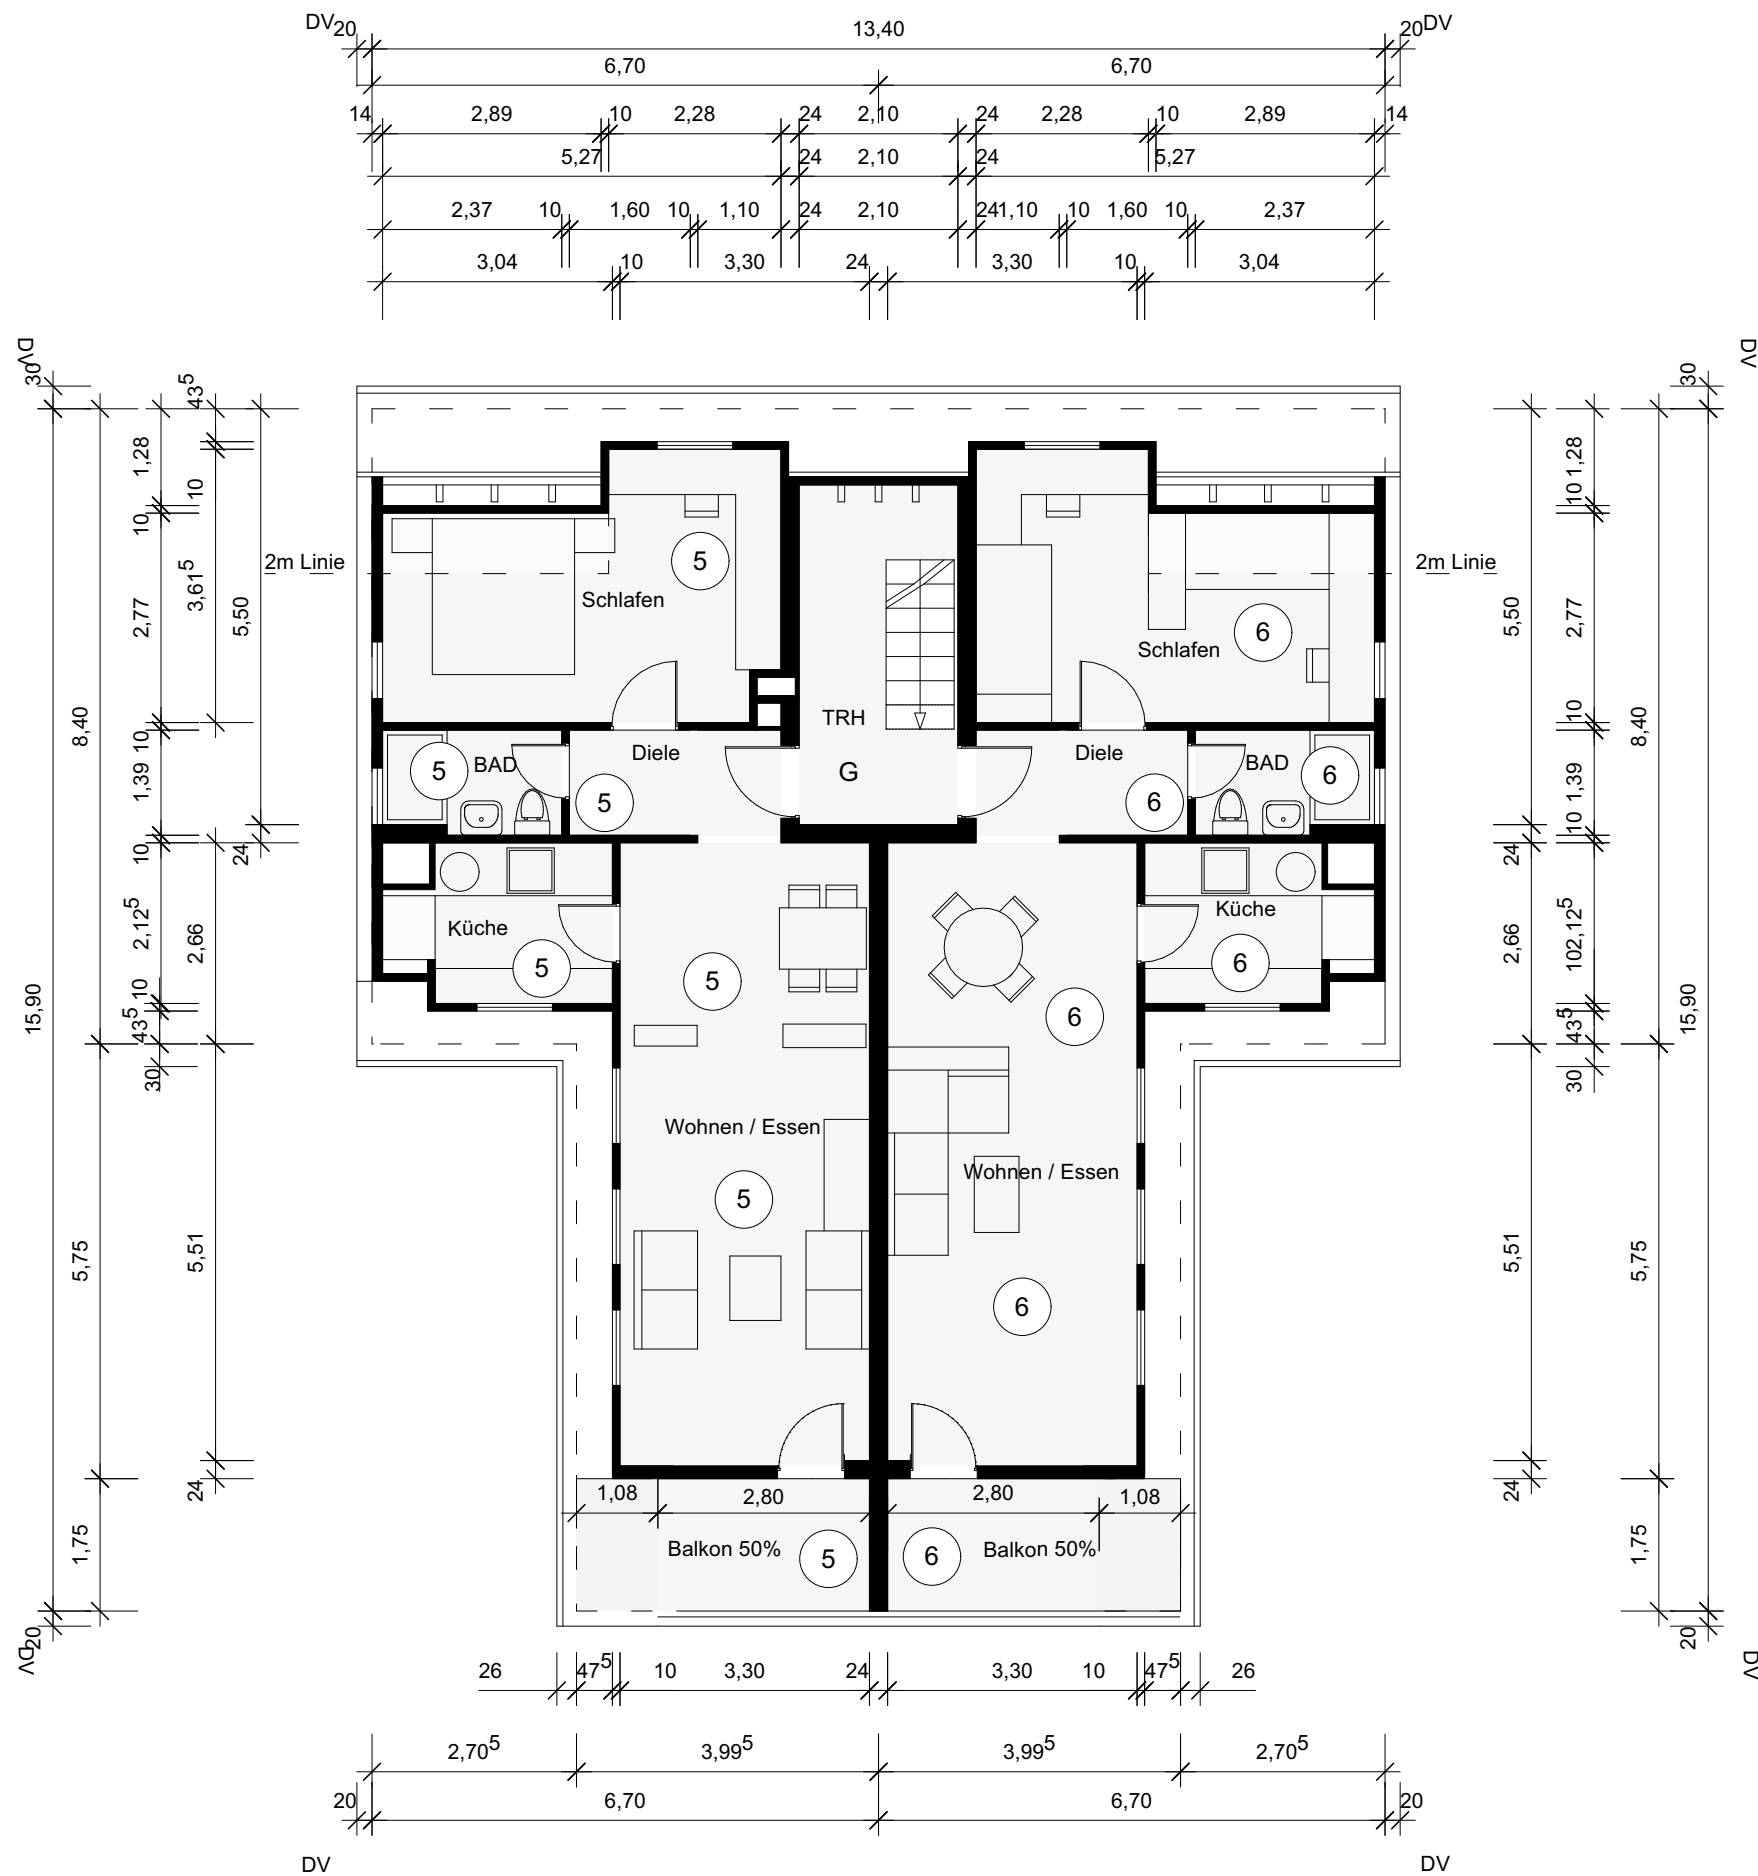



AUFTEILUNGSPLANUNG

Dachgeschoss

Art und Ort des Vorhabens: Aufteilung eines bestehenden Wohngebäudes mit 6 Wohneinheiten und 1 Garage und 6 PKW Außenstellplätze
Tulpenstraße 15
71063 Sindelfingen
Flst.-Nr.: 9495

Bauherr u. Antragsteller: Württemberger Wohnkonzepte GmbH
Ziegelstraße 1
73230 Kirchheim unter Teck
Vertreten durch die Geschäftsführung:
Dorothee Hahn & Marco Hans

Entwurfsverfasser: **jps architects**
Jean Pierre Schellhaas
Architekt
Krokusstraße 3
71034 Böblingen
Mitglied der AKBW
jp@jps-architects.com
0157 / 39 22 86 22

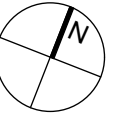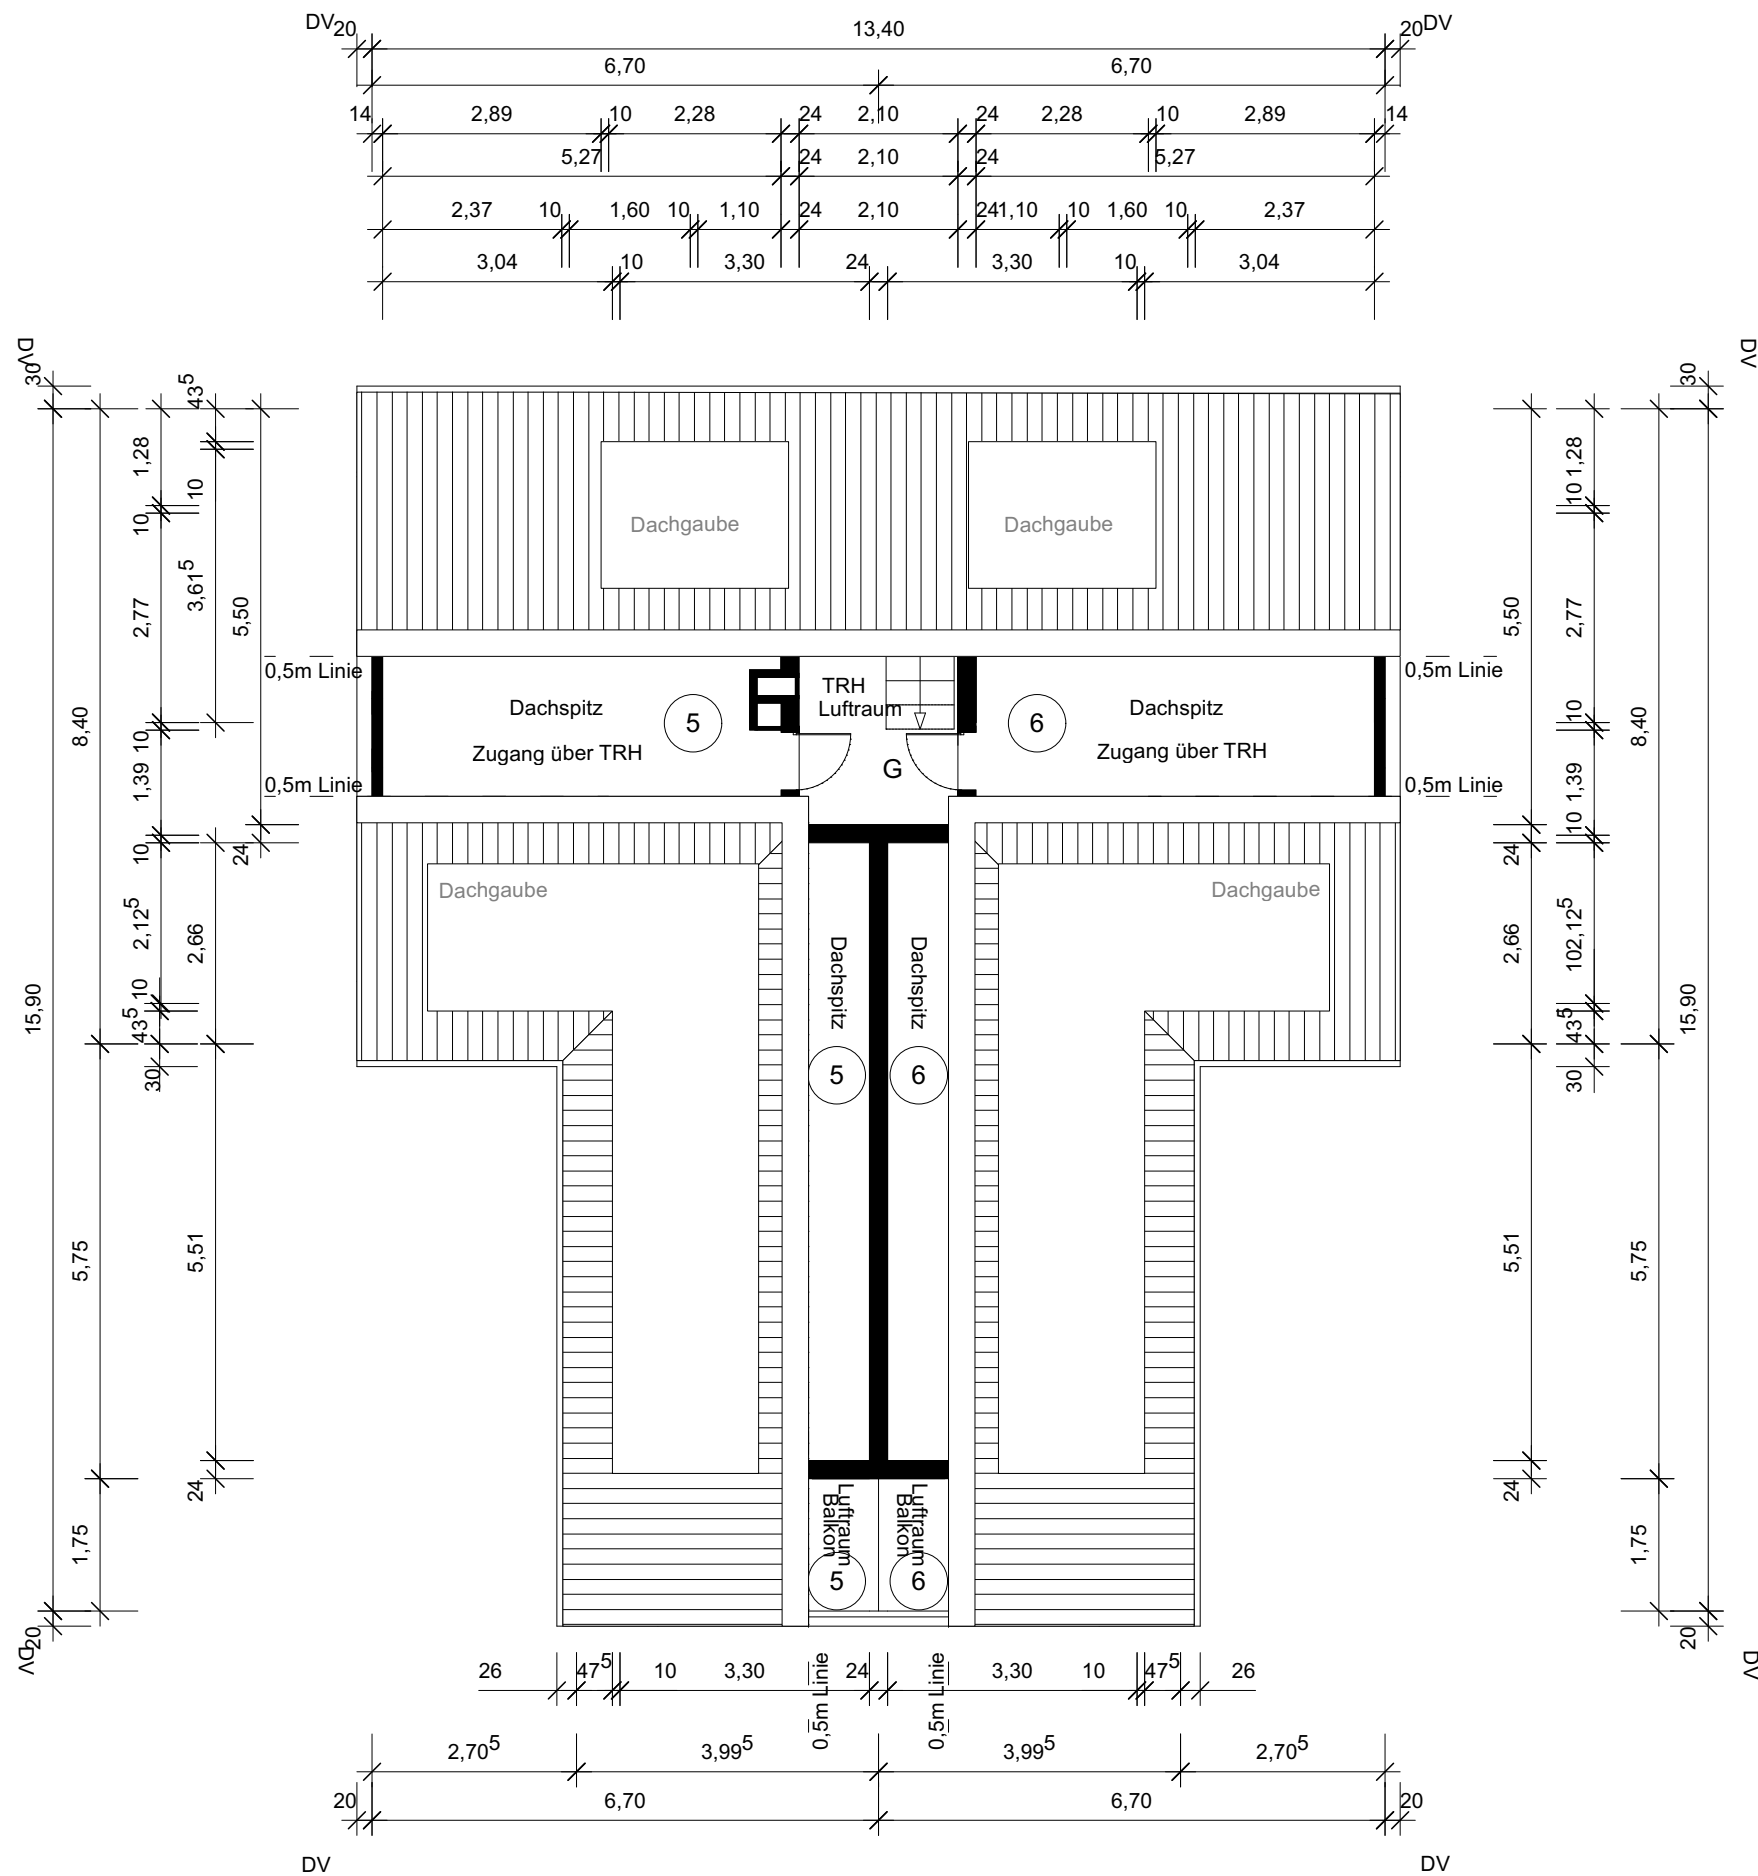

AUFTEILUNGSPLANUNG

Dachspitz

Art und Ort des Vorhabens: Aufteilung eines bestehenden Wohngebäudes mit 6 Wohneinheiten und 1 Garage und 6 PKW Außenstellplätze
Tulpenstraße 15
71063 Sindelfingen
Flst.-Nr.: 9495

Bauherr u. Antragsteller: Württemberger Wohnkonzepte GmbH
Ziegelstraße 1
73230 Kirchheim unter Teck
Vertreten durch die Geschäftsführung:
Dorothee Hahn & Marco Hans


Entwurfsverfasser: **jps architects**
Jean Pierre Schellhaas
Architekt
Krokusstraße 3
71034 Böblingen
Mitglied der AKBW
jp@jps-architects.com
0157 / 39 22 86 22



J. Pierre Schellhaas

Planstand: 04.08.2025

M 1:100

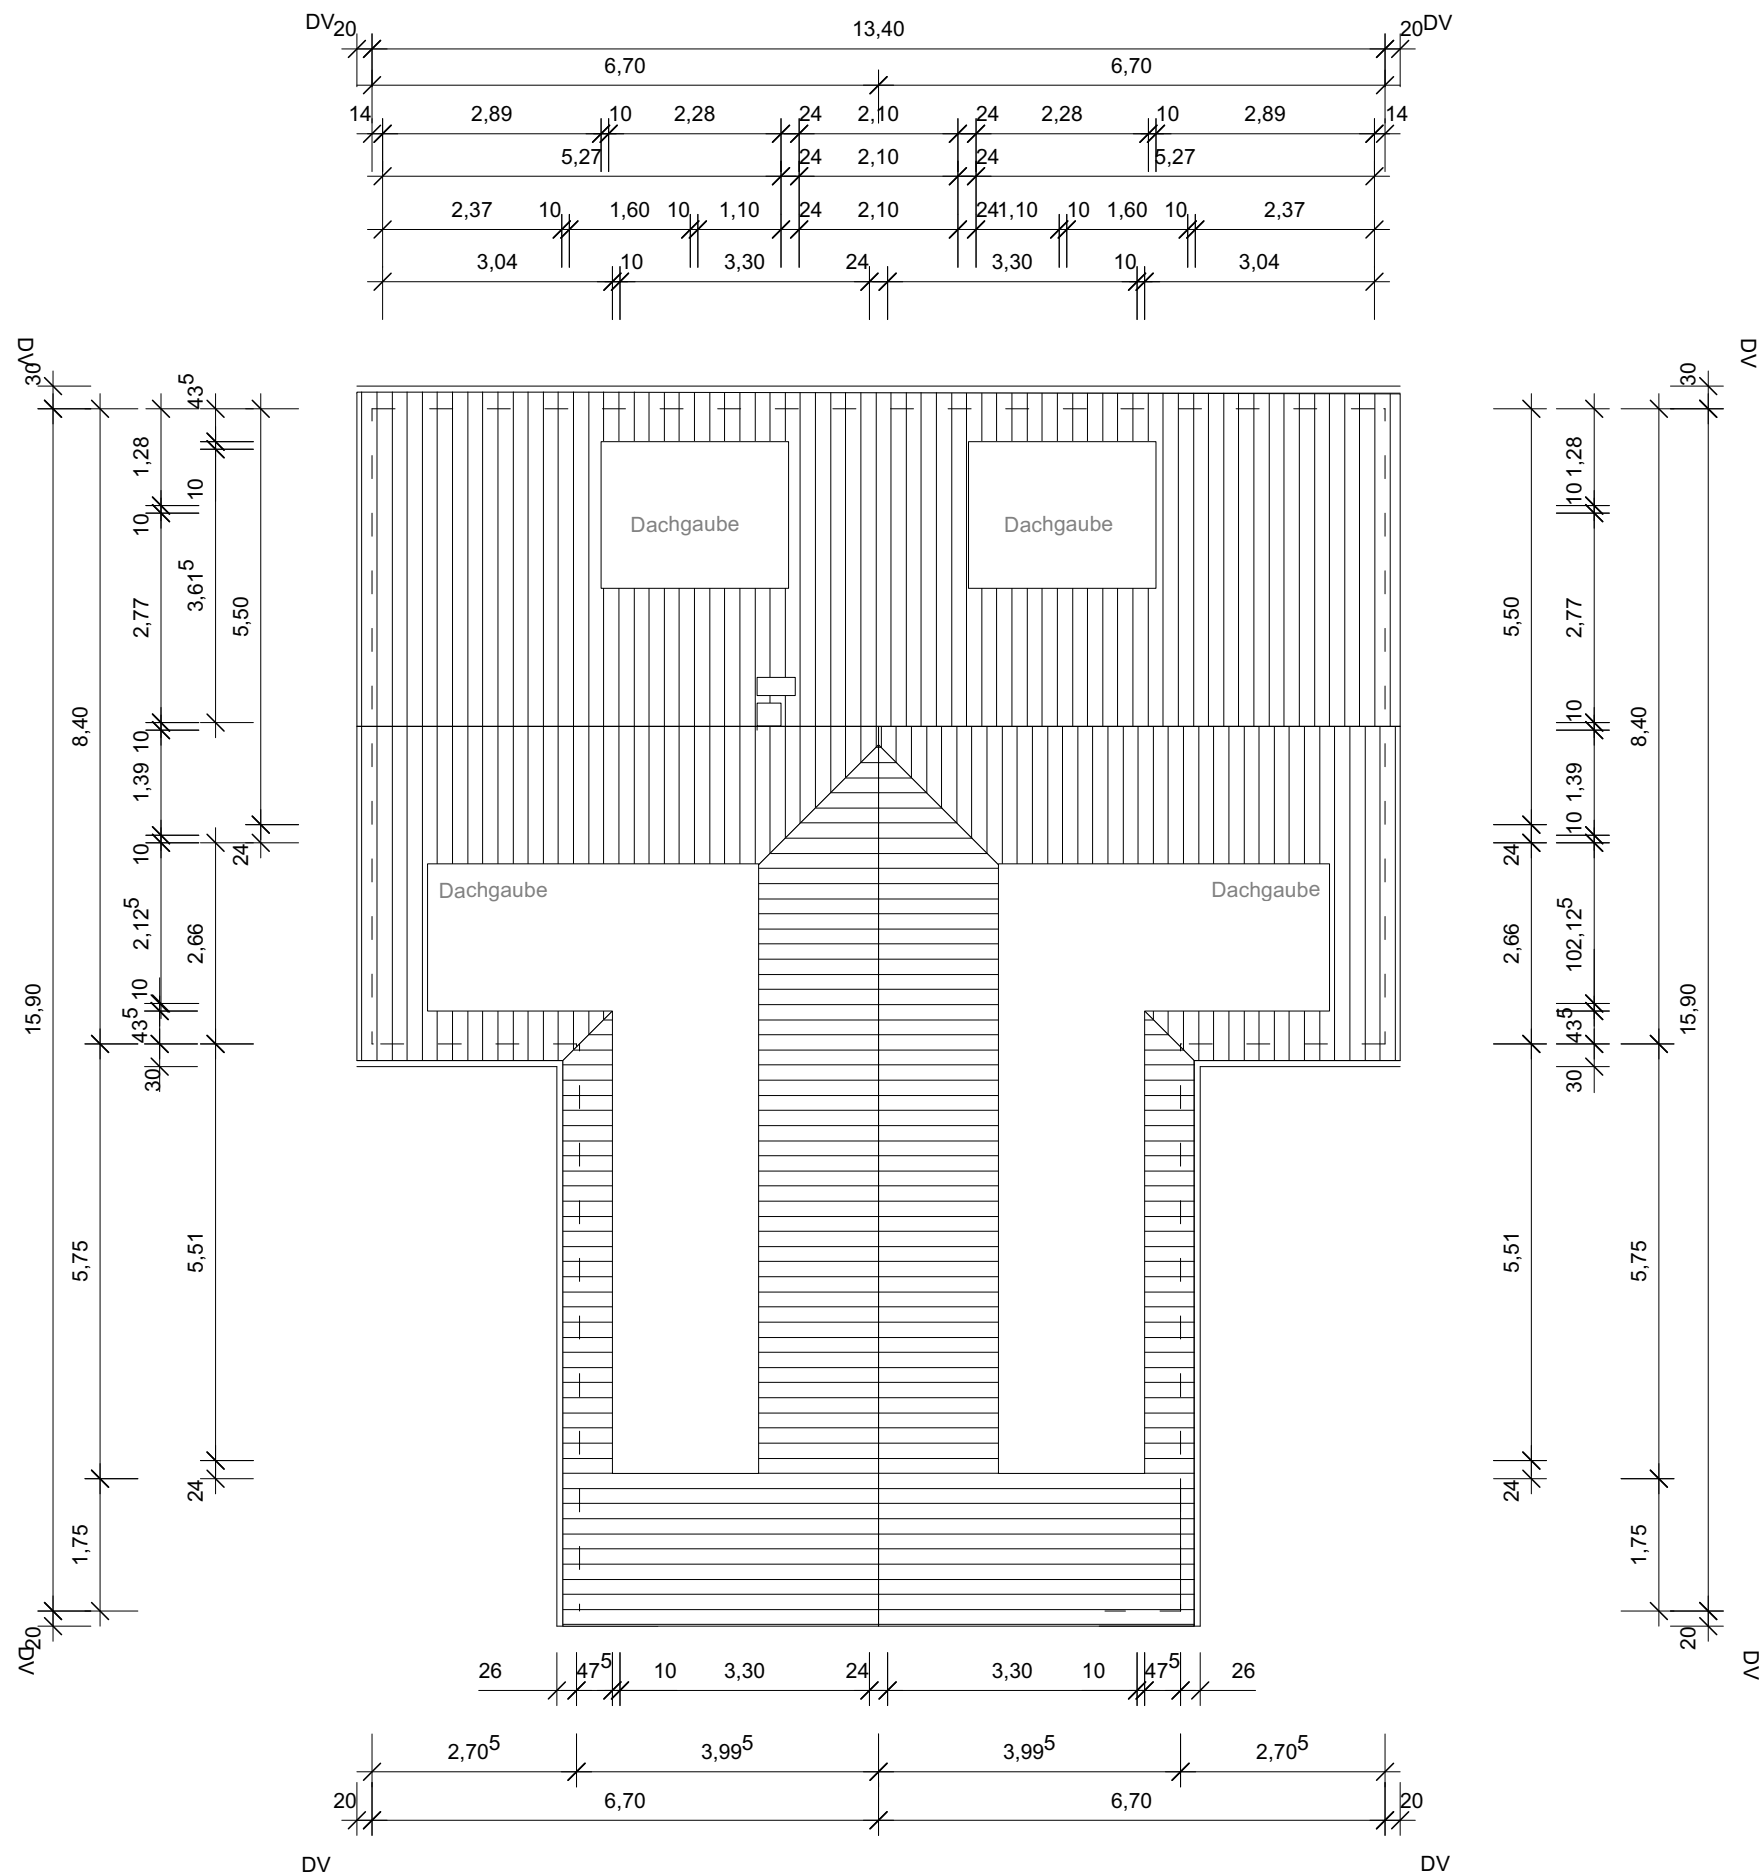

AUFTEILUNGSPLANUNG

Dachaufsicht

Art und Ort des Vorhabens: Aufteilung eines bestehenden Wohngebäudes mit 6 Wohneinheiten und 1 Garage und 6 PKW Außenstellplätze
Tulpenstraße 15
71063 Sindelfingen
Flst.-Nr.: 9495


Bauherr u. Antragsteller: Württemberger Wohnkonzepte GmbH
Ziegelstraße 1
73230 Kirchheim unter Teck
Vertreten durch die Geschäftsführung:
Dorothee Hahn & Marco Hans

Entwurfsverfasser: **jps architects**
Jean Pierre Schellhaas
Architekt
Krokusstraße 3
71034 Böblingen
Mitglied der AKBW
jp@jps-architects.com
0157 / 39 22 86 22


J.P. Schellhaas
J. Pierre Schellhaas

Planstand: 04.08.2025

M 1:100

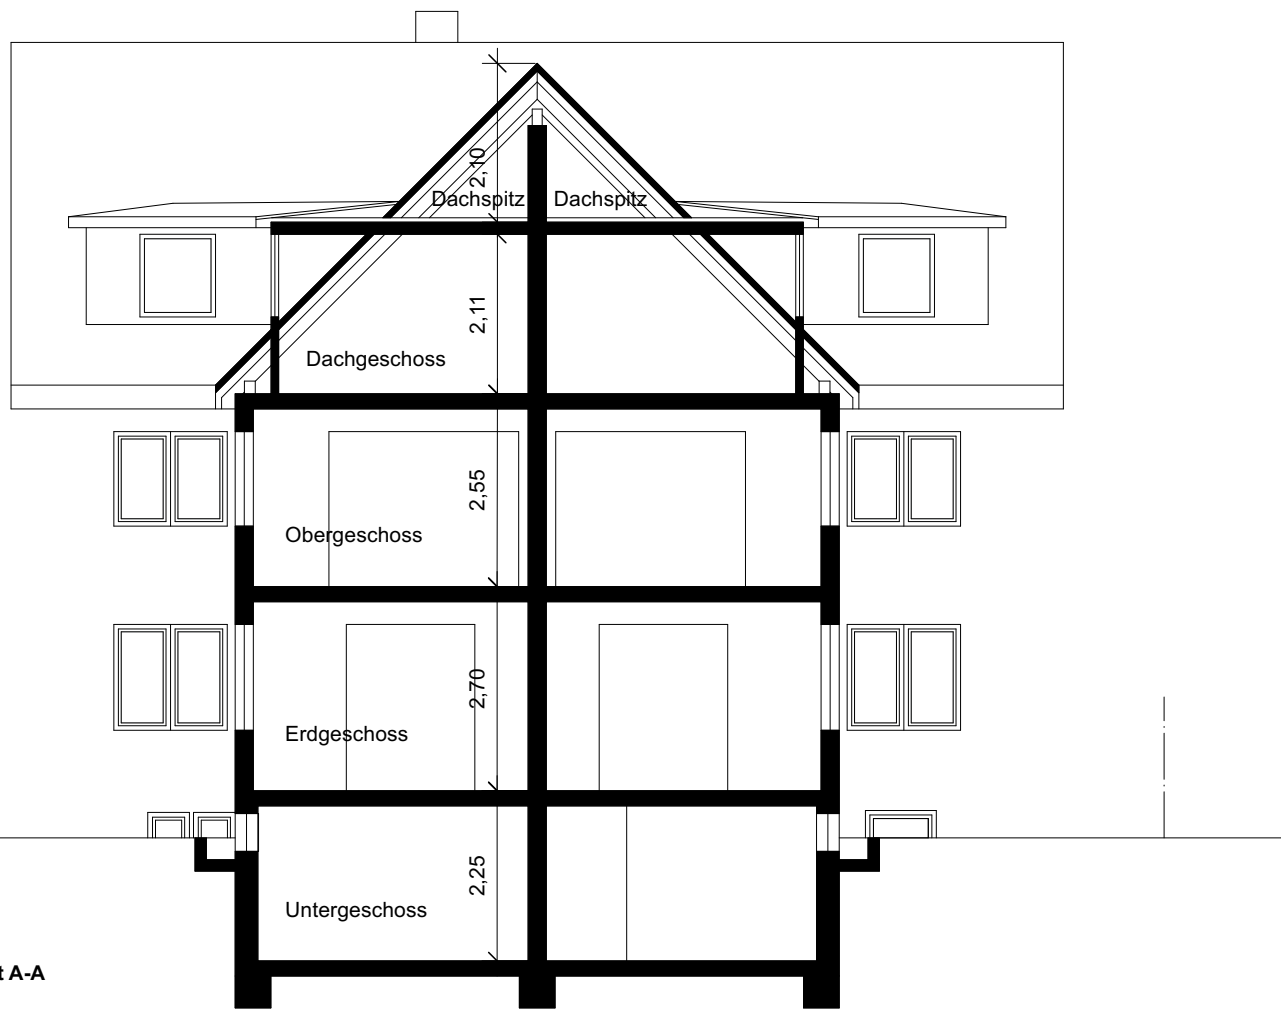

Schnitt A-A

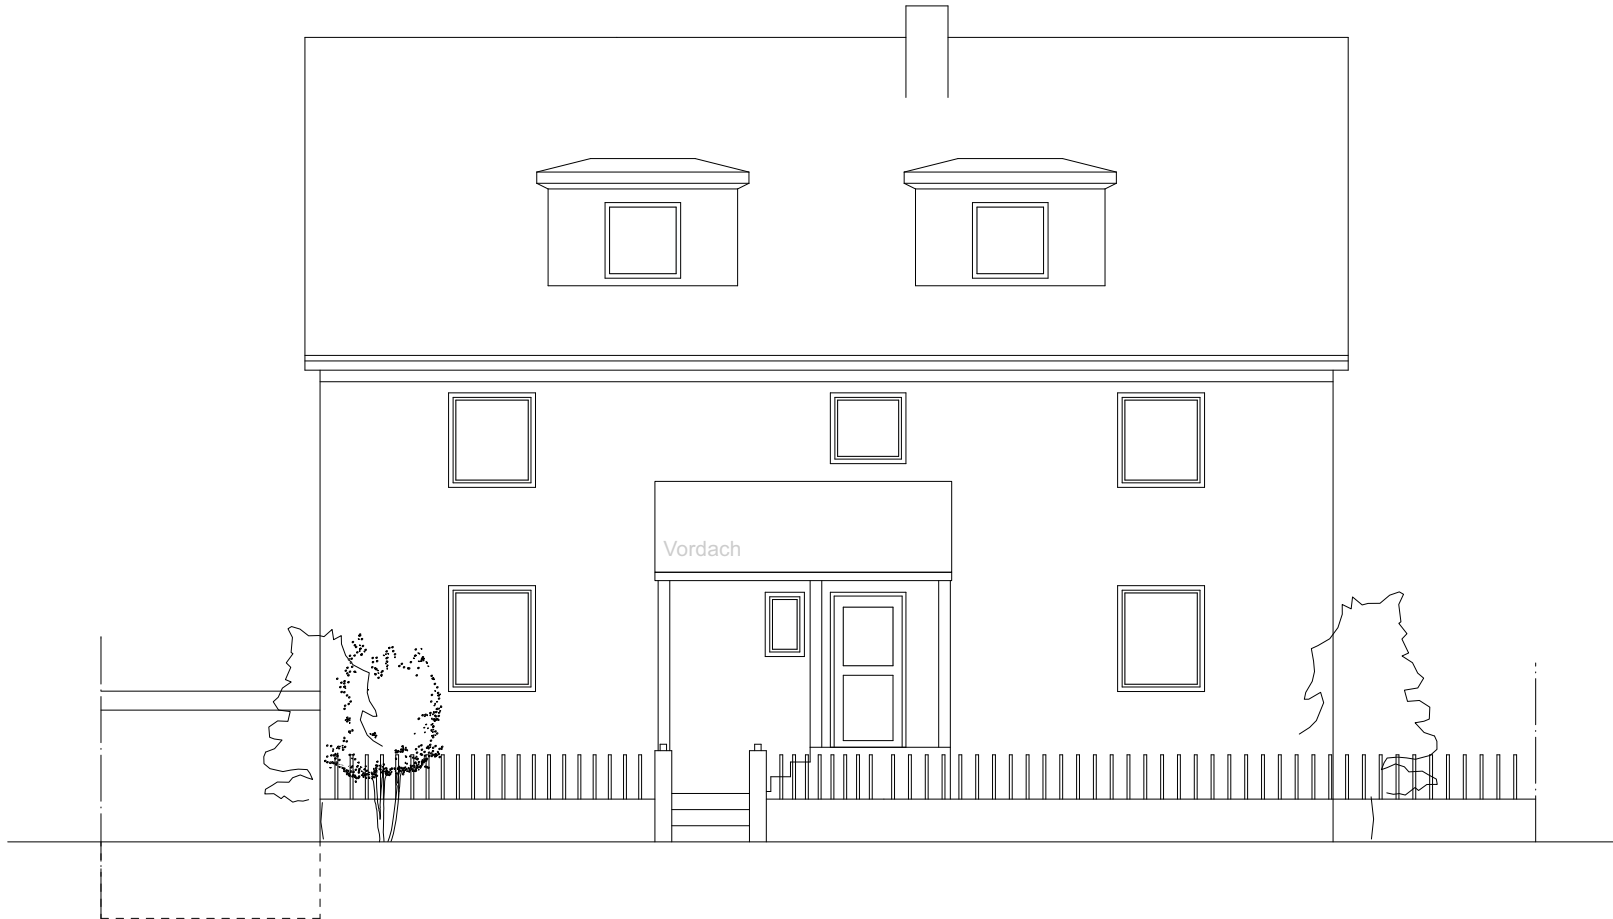

Ansicht Nordseite



Südseite

Ansicht Südseite

AUFTEILUNGSPLANUNG

Schnitt A-A + Ansicht Nordseite + Südseite

Art und Ort
des Vorhabens: Aufteilung eines bestehenden Wohngebäudes
mit 6 Wohneinheiten und 1 Garage und 6 PKW Außenstellplätze
Tulpenstraße 15
71063 Sindelfingen
Flst.-Nr.: 9495

Bauherr u.
Antragsteller: Württemberger Wohnkonzepte GmbH
Ziegelstraße 1
73230 Kirchheim unter Teck
Vertreten durch die Geschäftsführung:
Dorothee Hahn & Marco Hans

Entwurfsverfasser: **jps architects**
Jean Pierre Schellhaas
Architekt
Krokusstraße 3
71034 Böblingen
Mitglied der AKBW
jp@jps-architects.com
0157 / 39 22 86 22



J. Pierre Schellhaas

Planstand: 04.08.2025

M 1:100



Ansicht Westseite



Ansicht Ostseite

AUFTEILUNGSPLANUNG

Ansicht Westseite + Ostseite

Art und Ort
des Vorhabens:

Aufteilung eines bestehenden Wohngebäudes
mit 6 Wohneinheiten und 1 Garage und 6 PKW Außenstellplätze
Tulpenstraße 15
71063 Sindelfingen
Flst.-Nr.: 9495

Bauherr u.
Antragsteller:

Württembergischer Wohnkonzepte GmbH
Ziegelstraße 1
73230 Kirchheim unter Teck
Vertreten durch die Geschäftsführung:
Dorothee Hahn & Marco Hans

Entwurfsverfasser:



jps architects
Jean Pierre Schellhaas
Architekt
Krokusstraße 3
71034 Böblingen
Mitglied der AKBW



jp@jps-architects.com
0157 / 39 22 86 22

Planstand: 04.08.2025

M 1:100