


Landkreis : Böblingen
Gemeinde : Sindelfingen
Gemarkung : Sindelfingen

LAGEPLAN

Zeichnerischer Teil zum
Bauantrag (§ 2 BauVorIVO)

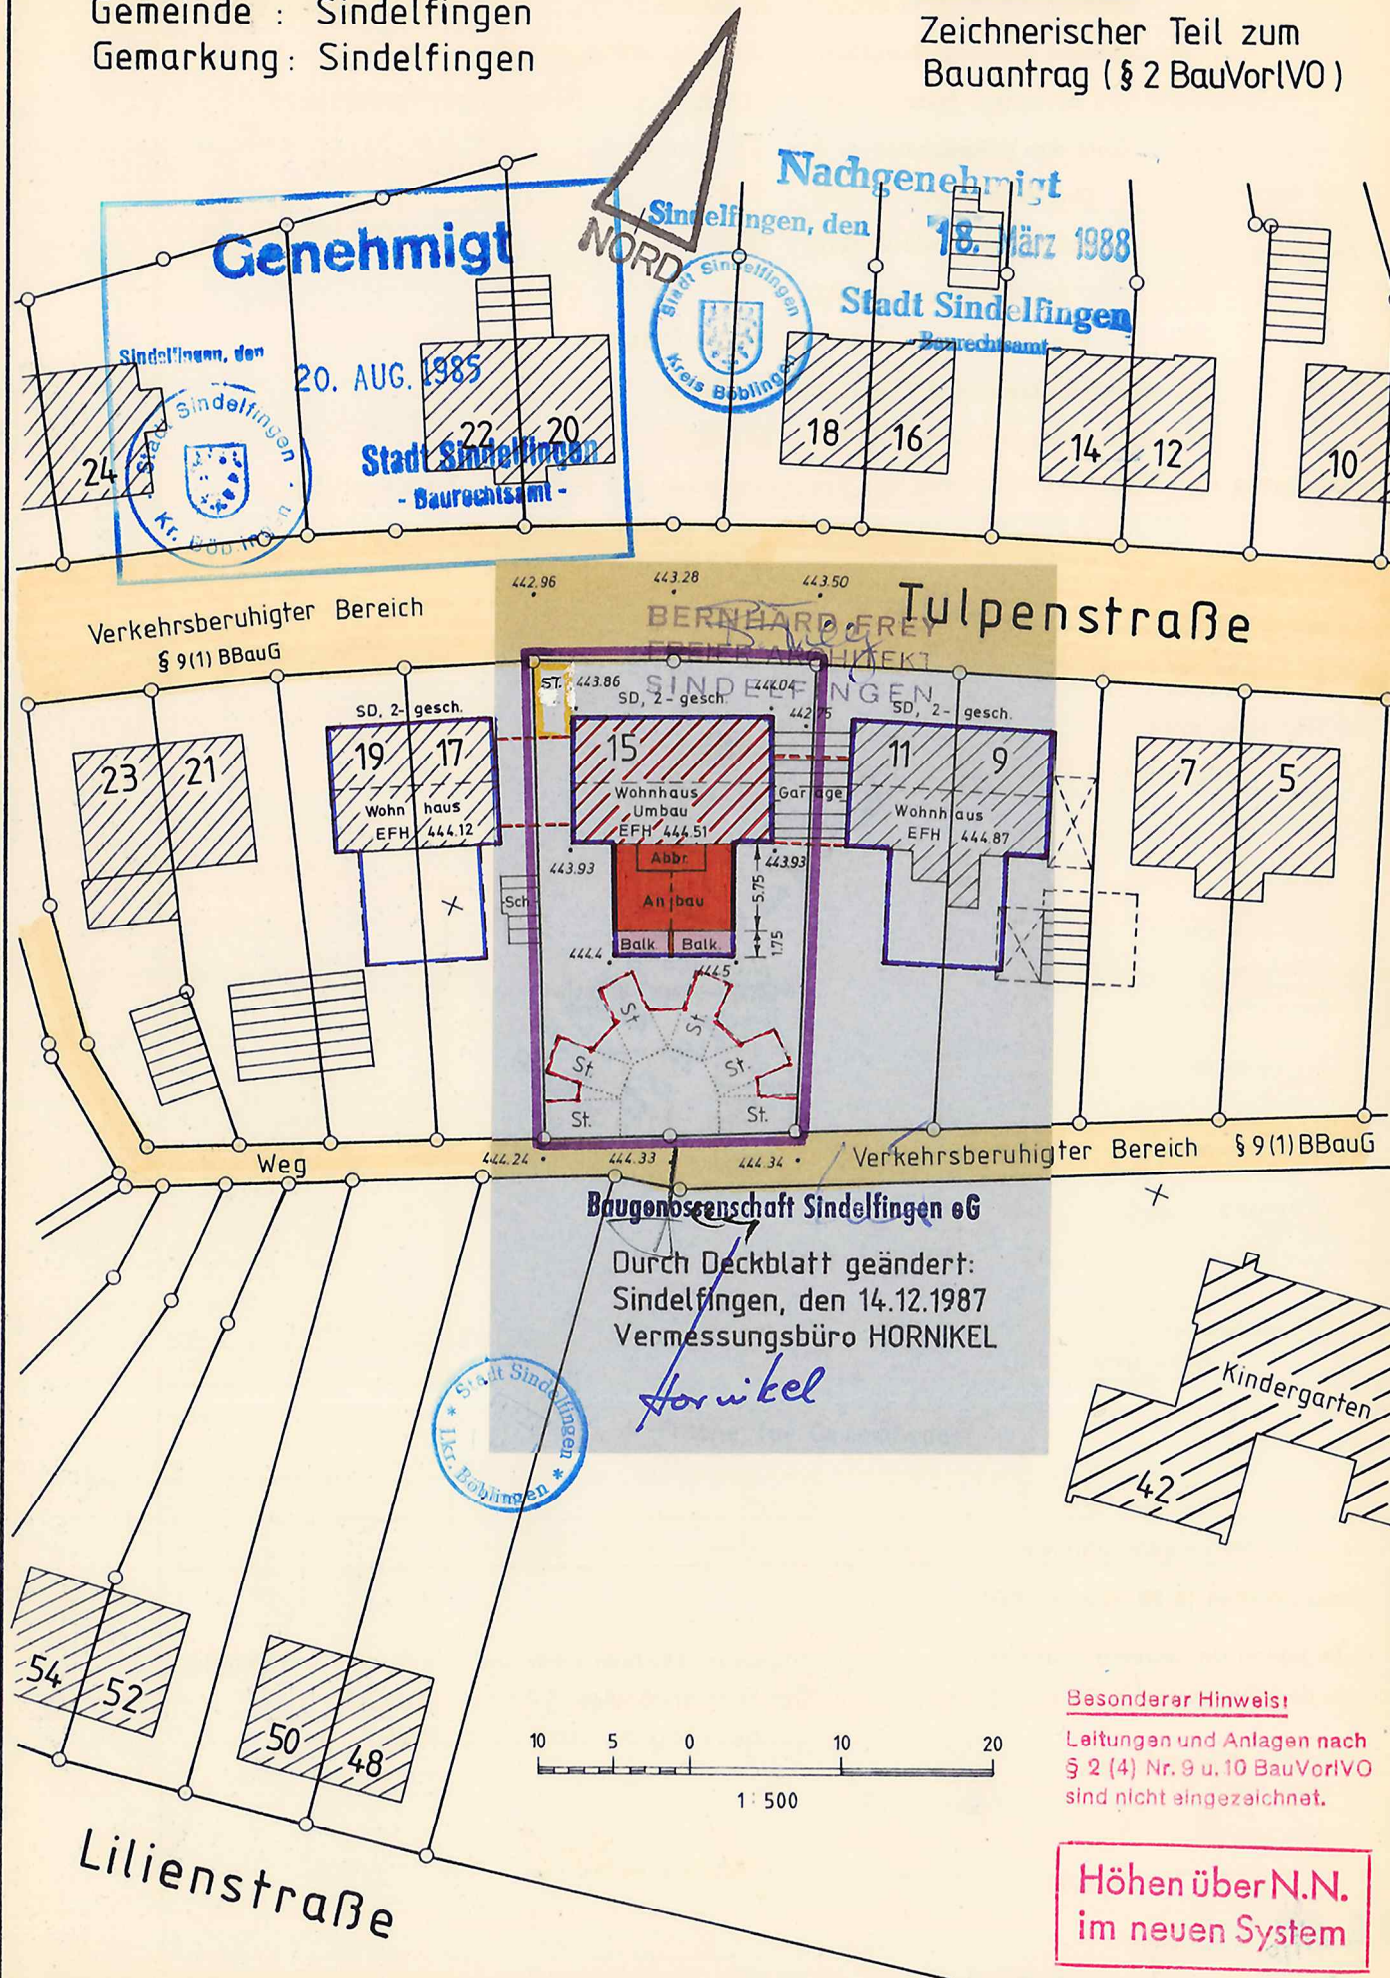

Vermessungsbüro Heinz Hornikel, Wolboldstraße 3, 7032 Sindelfingen, Telefon 87 59 66

Festsetzungen des Bebauungsplanes und der örtlichen Bauvorschriften (§ 2 Abs. 6 Nr. 5 BauVorIVO)

- 8.1 Bebauungsplan (Name u. Reg.Nr.): Zimmerplatzsiedlung
- 8.2 rechtsverbindlich (§ 12 BBauG): JA / ~~XXXX~~ seit: 13.6.65
- 8.3 Art der baulichen Nutzung (Baugebiet): Reines Wohngebiet
- 8.4 Ausnahmen und besondere Festsetzungen: XX / NEIN Bebauungsplanentwurf 2. Änderung v. 16.5.85
- 8.5.1 Zahl der Vollgeschosse = Z: II Der rechtsgültige Bebauungsplan v. 13.6.65 ist im zeichnerischen Teil des Lageplans nicht dargestellt.
- 8.5.2 Maß der baulichen Nutzung Grundflächenzahl = GRZ: 0,4
- 8.5.3 Geschosflächenzahl = GFZ: 0,8
- 8.5.4 Baumassenzahl = BMZ: ---
- 8.6 Bauweise (§ 22 BauNVO): Doppelhäuser
- 8.7 Sonstige Festsetzungen (§ 9 BBauG): JA / ~~XXXX~~
- 8.8 Örtliche Bauvorschriften (§ 111 LBO): XX / NEIN
- 9 Berechnung der Flächenbeanspruchung des Baugrundstückes (§ 2 Abs. 6 Nr. 7 BauVorIVO)
- 9.1 Fläche des Baugrundstückes: 552 qm
- 9.1.1 zu Zuschlag nach § 21a Abs. 2 BauNVO : + --- qm
- 9.1.2 ab Fläche vor der Straßenbegrenzungslinie : --- --- qm
- 9.1.3 ab Teilflächen des Baugrundstückes, die nicht im Bauland liegen (§ 19 Abs. 3 BauNVO) : --- --- qm
- 9.1.4 ab Flächenbaulasten : --- --- qm
- 9.2 Maßgebende Grundstücksfläche = MGF 552 qm

	bauliche Grundfläche	Geschosfläche	Baumasse
9.3 baul. Nutzung d. Baugrundstückes			
9.4.1 baul. Anlagen vorhanden	113 qm	225 qm	cbm
9.4.2 baul. Anlagen (ohne Garagen und überdachte Stellplätze) geplant	46 qm	219 qm	cbm
9.5.1 Garagen und überdachte Stellplätze vorhanden	17 qm	17 qm	cbm
9.5.2 Garagen und überdachte Stellplätze geplant	-- qm	-- qm	cbm
9.6 vorhanden + geplant	17 qm	17 qm	cbm
9.7 Nach § 21a Abs. 3 S. 1 BauNVO ab 0,1 x MGF	55 qm		
9.8 verbleiben	-- qm		
9.9 anzurechnen unter Berücksichtigung von § 21a in Anspruch genommen	159 qm	444 qm	cbm
9.10 MGF x GRZ =	221 qm	442 qm	cbm
9.11 MGF x GFZ =	442 qm	442 qm	cbm
9.12 zulässige Nutzung	221 qm	442 qm	cbm
9.13 zulässige Nutzung überschritten zu --- qm = --- % zu 2 qm = 0,5 % zu --- qm = --- %			

Unterschriften (§ 90 Abs. 4 LBO)

Das im Lageplan dargestellte Vorhaben entspricht dem Bauantrag (§ 79 Abs. 1 LBO)

Lageplan zeichnerischer und schriftlicher Teil gefertigt.
Der Sachverständige (§ 79 Abs. 2 LBO)
Sindelfingen, den 24.6.1985

Planverfasser:

5.7.85 B. Frey
Datum Unterschrift

16. JULI 1985 Bauherr:

Baugewerkschaft Sindelfingen eG
Datum Unterschrift

Bearbeitungs-
vermerke

Stadt — Landkreis: Böblingen

Gemeinde: Sindelfingen

Gemarkung: Sindelfingen

LAGEPLAN

— SCHRIFTLICHER TEIL —
zum Bauantrag (§ 2 BauVorIVO)

1 Bauherr (Name und Anschrift)	Baugewerkschaft Sindelfingen eG. Lützelwiesenstr. 19, 7032 Sindelfingen	Bearbeitungs- vermerke
2 Bauliche Nutzung des Baugrundstückes (§ 2 Abs. 6 Nr. 6 BauVorIVO)	geplant vorhanden An- und Umbau der bestehenden Wohnhäuser Wohnhäuser, Garage	
3 Baugrundstück (§ 2 Abs. 6 Nr. 1 BauVorIVO)	Flurstück(e) Nr. Grundbuch Fläche Tulpenstr. 13 3070/250 275 m ² Tulpenstr. 15 3070/251 277 m ²	
4 Eigentümer lt. Grundbuch mit Anschrift (§ 2 Abs. 6 Nr. 1 BauVorIVO)	Baugewerkschaft Sindelfingen eG. Lützelwiesenstr. 19, 7032 Sindelfingen	
5 Baulasten und sonstige öffentl. Lasten oder Beschränkungen mit Fundstelle (§ 2 Abs. 6 Nr. 2 BauVorIVO)	-----	
6 Bemerkungen und Hinweis auf Schutzraumbauten (§ 2 Abs. 6 Nr. 4 BauVorIVO)	Die Vereinigung der beiden Grundstücke wird beantragt.	
7 Nachbargrundstücke Flurstück Nr.	(§ 2 Abs. 6 Nr. 2 BauVorIVO) Eigentümer lt. Grundbuch mit Anschrift	
Tulpenstr. 11	Stefan und Anna Kunz Tulpenstr. 11, 7032 Sindelfingen	
Tulpenstr. 17	Karl Eberspächer Maichinger Str. 14, 7032 Sindelfingen	

1) Nichtzutreffendes streichen